



- NOTES :**  
THIS DRAWING IS SUBJECTED TO COPYRIGHT AND CANNOT BE COPIED WITHOUT ANY PRIOR WRITTEN CONSENT BY THE COPIER TO THE ARCHITECT FOR APPROVAL  
THE CONTRACTOR SHALL VERIFY THE ALL DIMENSIONS IN DRAWING TO THE SITE IN RESPECTIVE SCALE. MENTIONED IN DRAWING AND DRAWING MUST BE REFERRED TO THE ARCHITECT IF ANY DISCREPANCIES ARE NOTICED IN DRAWING BEFORE COMMENCEMENT OR DURING EXECUTION .
1. ALL THE DIMENSIONS ARE IN IMPERIAL SCALE UNLESS AND UNTIL MENTIONED BY THE CONTRACTOR FOR CHANGE OF UNITS.
  2. THE DRAWING SHOULD BE READ AND NOT BE MEASURED.
  3. ANY DEVIATION FROM THE CONSTRUCTION DRAWINGS, THE CONTRACTOR/ SUB CONTRACTOR SHOULD GET AN APPROVAL FROM THE CONCERNED ARCHITECT OR ENGINEER BEFORE THE COMMENCEMENT OF CONSTRUCTION.
  4. ALL ARCHITECTURAL DRAWINGS MUST BE REFERRED IN COORDINATION WITH STRUCTURAL DRAWINGS.

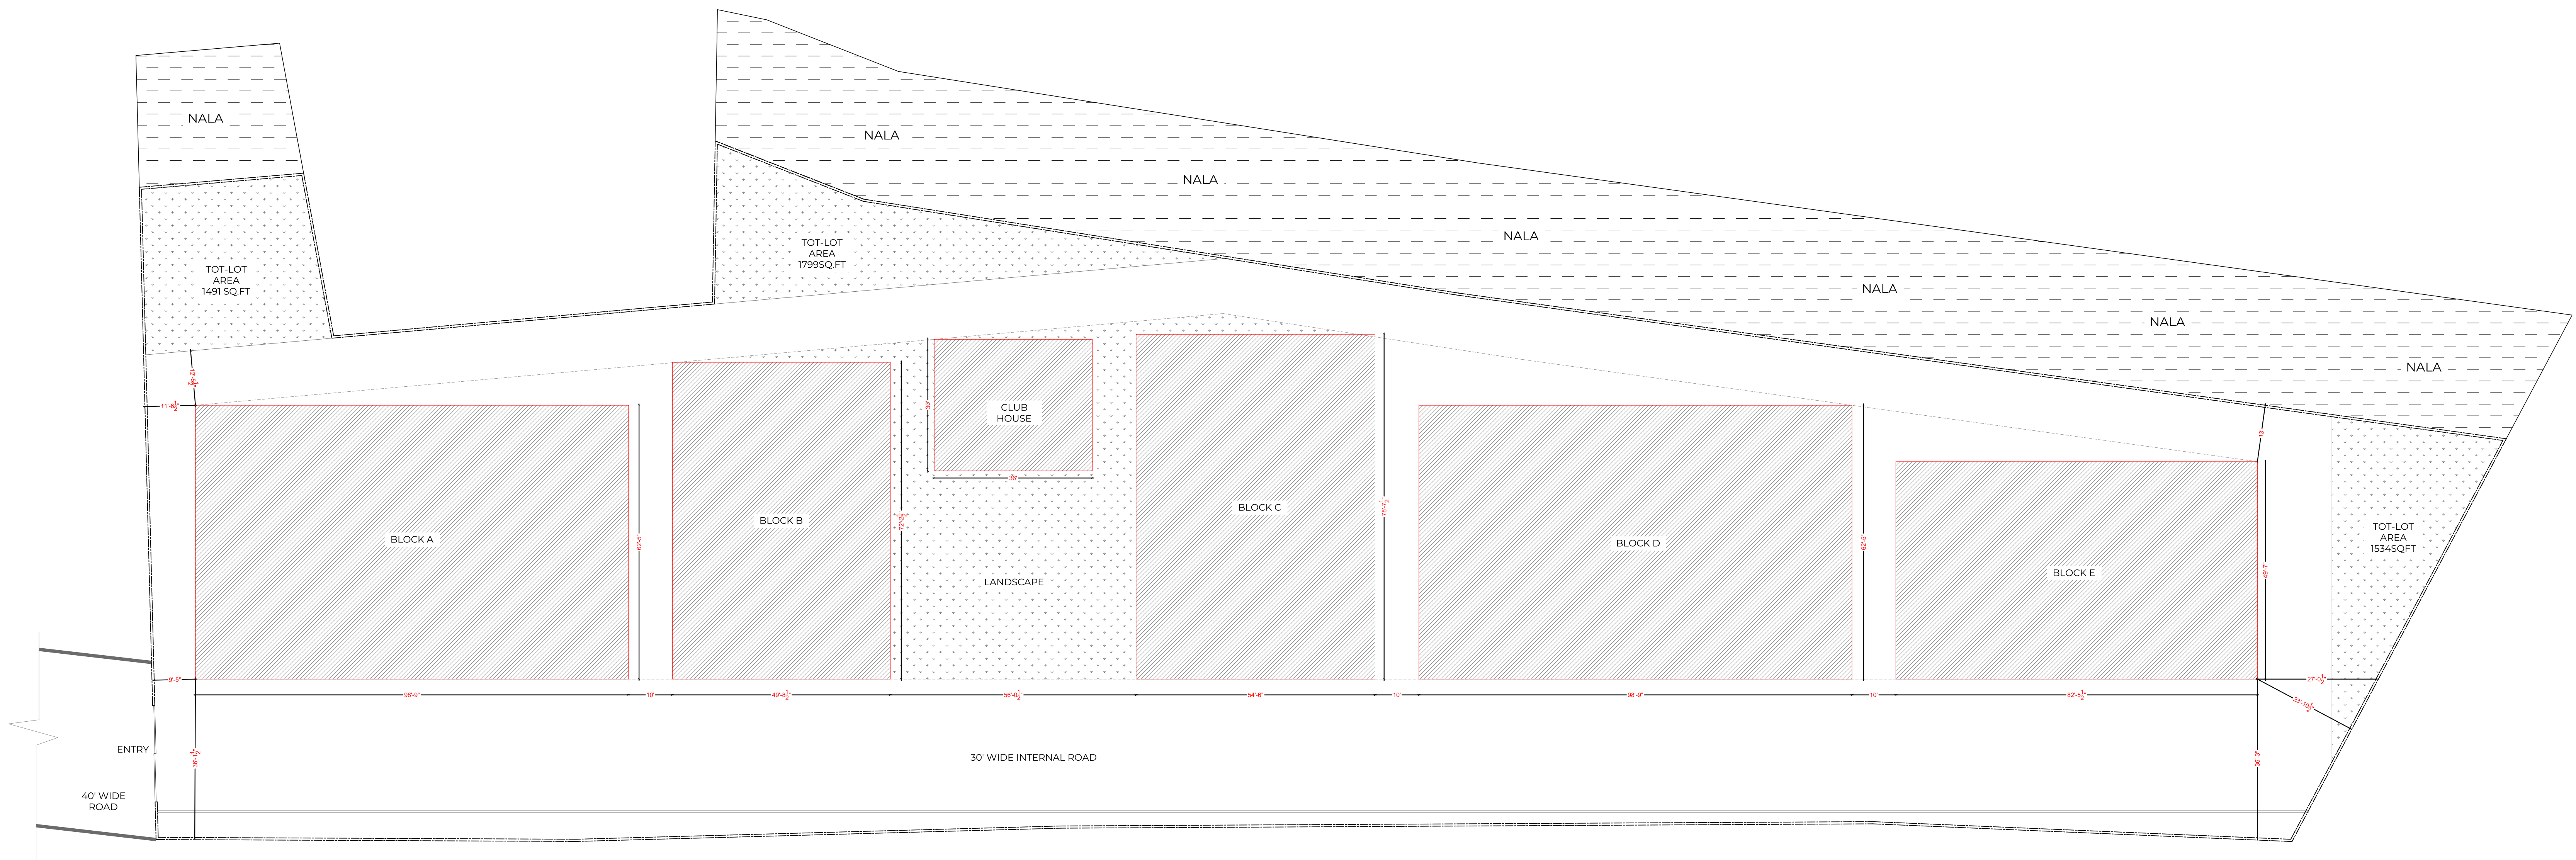


|                                                        |               |                                                                                       |               |
|--------------------------------------------------------|---------------|---------------------------------------------------------------------------------------|---------------|
| DRAWING TITLE : SITE PLAN                              |               |  |               |
| PROJECT TITLE : SERVICE APARTMENT @NALAGANDLA          |               |                                                                                       |               |
| DWG. No. : -                                           |               | DWG. STG. : DESIGN DEVELOPMENT                                                        |               |
| CLIENT : Mr.MAHENDAR REDDY                             |               | LOCATION : NALAGANDLA,HYD                                                             |               |
| ARCHITECT: CHANDRASHEKAR                               |               | DRAWN BY: AR.AJAYSAI                                                                  |               |
| SCALE NTS                                              | DATE 7-Apr-26 | REVISION : 001                                                                        | APPROVED: CSY |
| COUNT OF TOTAL NO. OF DRWGS. ISSUED TO SITE / CLIENT : |               |                                                                                       | 001           |

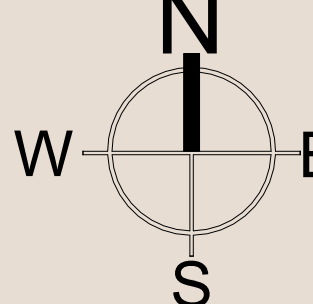

**NOTES :**


THIS DRAWING IS SUBJECT TO COPYRIGHT AND CANNOT BE COPIED WITHOUT ANY PRIOR WRITTEN CONSENT BY THE COPIER TO THE ARCHITECT FOR APPROVAL  
THE CONTRACTOR SHALL VERIFY THE ALL DIMENSIONS IN DRAWING TO THE SITE IN RESPECTIVE SCALE. MENTIONED IN DRAWING AND DRAWING MUST BE REFERRED TO THE ARCHITECT IF ANY DISCREPANCIES ARE NOTICED IN DRAWING BEFORE COMMENCEMENT OR DURING EXECUTION .

1. ALL THE DIMENSIONS ARE IN IMPERIAL SCALE UNLESS AND UNTIL MENTIONED BY THE CONTRACTOR FOR CHANGE OF UNITS.
2. THE DRAWING SHOULD BE READ AND NOT BE MEASURED.
3. ANY DEVIATION FROM THE CONSTRUCTION DRAWINGS, THE CONTRACTOR/ SUB CONTRACTOR SHOULD GET AN APPROVAL FROM THE CONCERNED ARCHITECT OR ENGINEER BEFORE THE COMMENCEMENT OF CONSTRUCTION.
4. ALL ARCHITECTURAL DRAWINGS MUST BE REFERRED IN COORDINATION WITH STRUCTURAL DRAWINGS.

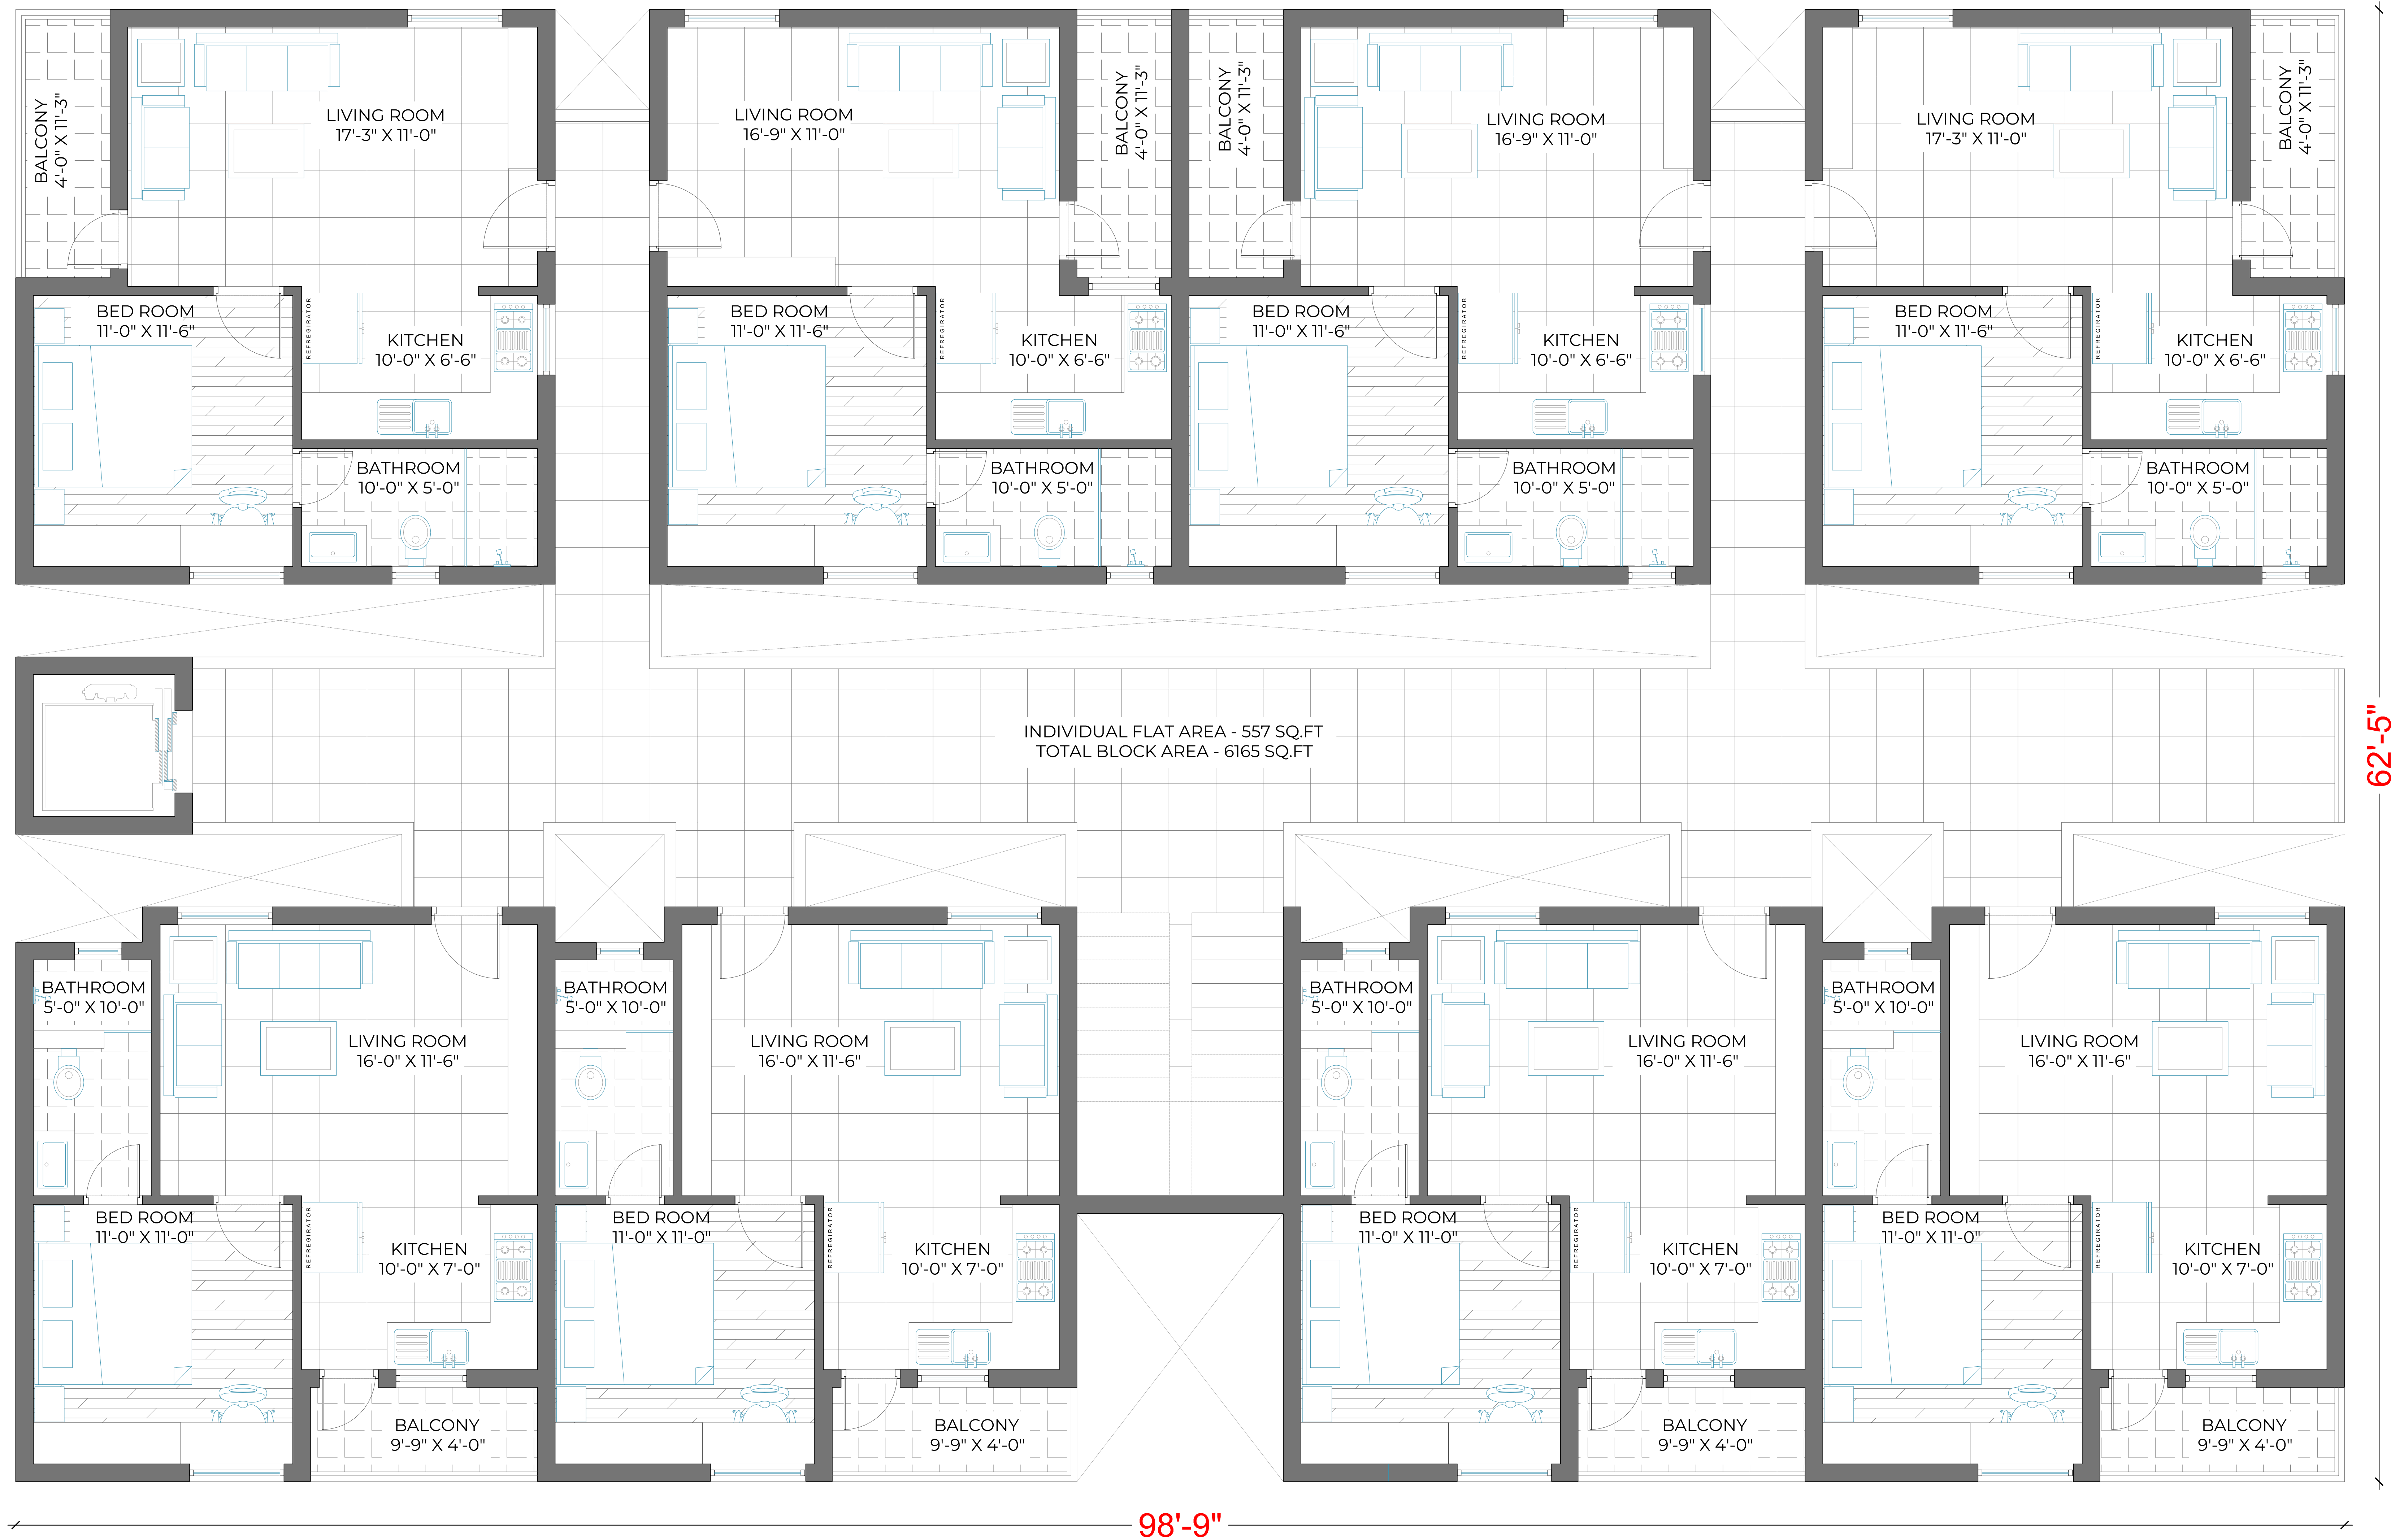

**DRAWING TITLE :** BLOCK A TYPICAL FLOOR  
PLAN

**PROJECT TITLE :** SERVICE APARTMENT  
@NALAGANDLA

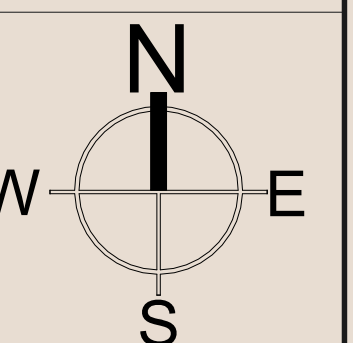

DWG. No. : - DWG. STG. : DESIGN DEVELOPMENT

CLIENT : Mr.MAHENDAR REDDY LOCATION : NALAGANDLA, HYD

ARCHITECT: CHANDRASHEKAR DRAWN BY: AR.AJAYSAI

SCALE NTS DATE 7-Apr-26 REVISION : 001 APPROVED: CSY


COUNT OF TOTAL NO. OF DRWGS. ISSUED TO SITE / CLIENT : 002



**NOTES :**


THIS DRAWING IS SUBJECT TO COPYRIGHT AND CANNOT BE COPIED WITHOUT ANY PRIOR WRITTEN CONSENT BY THE COPIER TO THE ARCHITECT FOR APPROVAL. THE CONTRACTOR SHALL VERIFY THE ALL DIMENSIONS IN DRAWING TO THE SITE IN RESPECTIVE SCALE. MENTIONED IN DRAWING AND DRAWING MUST BE REFERRED TO THE ARCHITECT IF ANY DISCREPANCIES ARE NOTICED IN DRAWING BEFORE COMMENCEMENT OR DURING EXECUTION.

1. ALL THE DIMENSIONS ARE IN IMPERIAL SCALE UNLESS AND UNTIL MENTIONED BY THE CONTRACTOR FOR CHANGE OF UNITS.
2. THE DRAWING SHOULD BE READ AND NOT BE MEASURED.
3. ANY DEVIATION FROM THE CONSTRUCTION DRAWINGS, THE CONTRACTOR/ SUB CONTRACTOR SHOULD GET AN APPROVAL FROM THE CONCERNED ARCHITECT OR ENGINEER BEFORE THE COMMENCEMENT OF CONSTRUCTION.
4. ALL ARCHITECTURAL DRAWINGS MUST BE REFERRED IN COORDINATION WITH STRUCTURAL DRAWINGS.

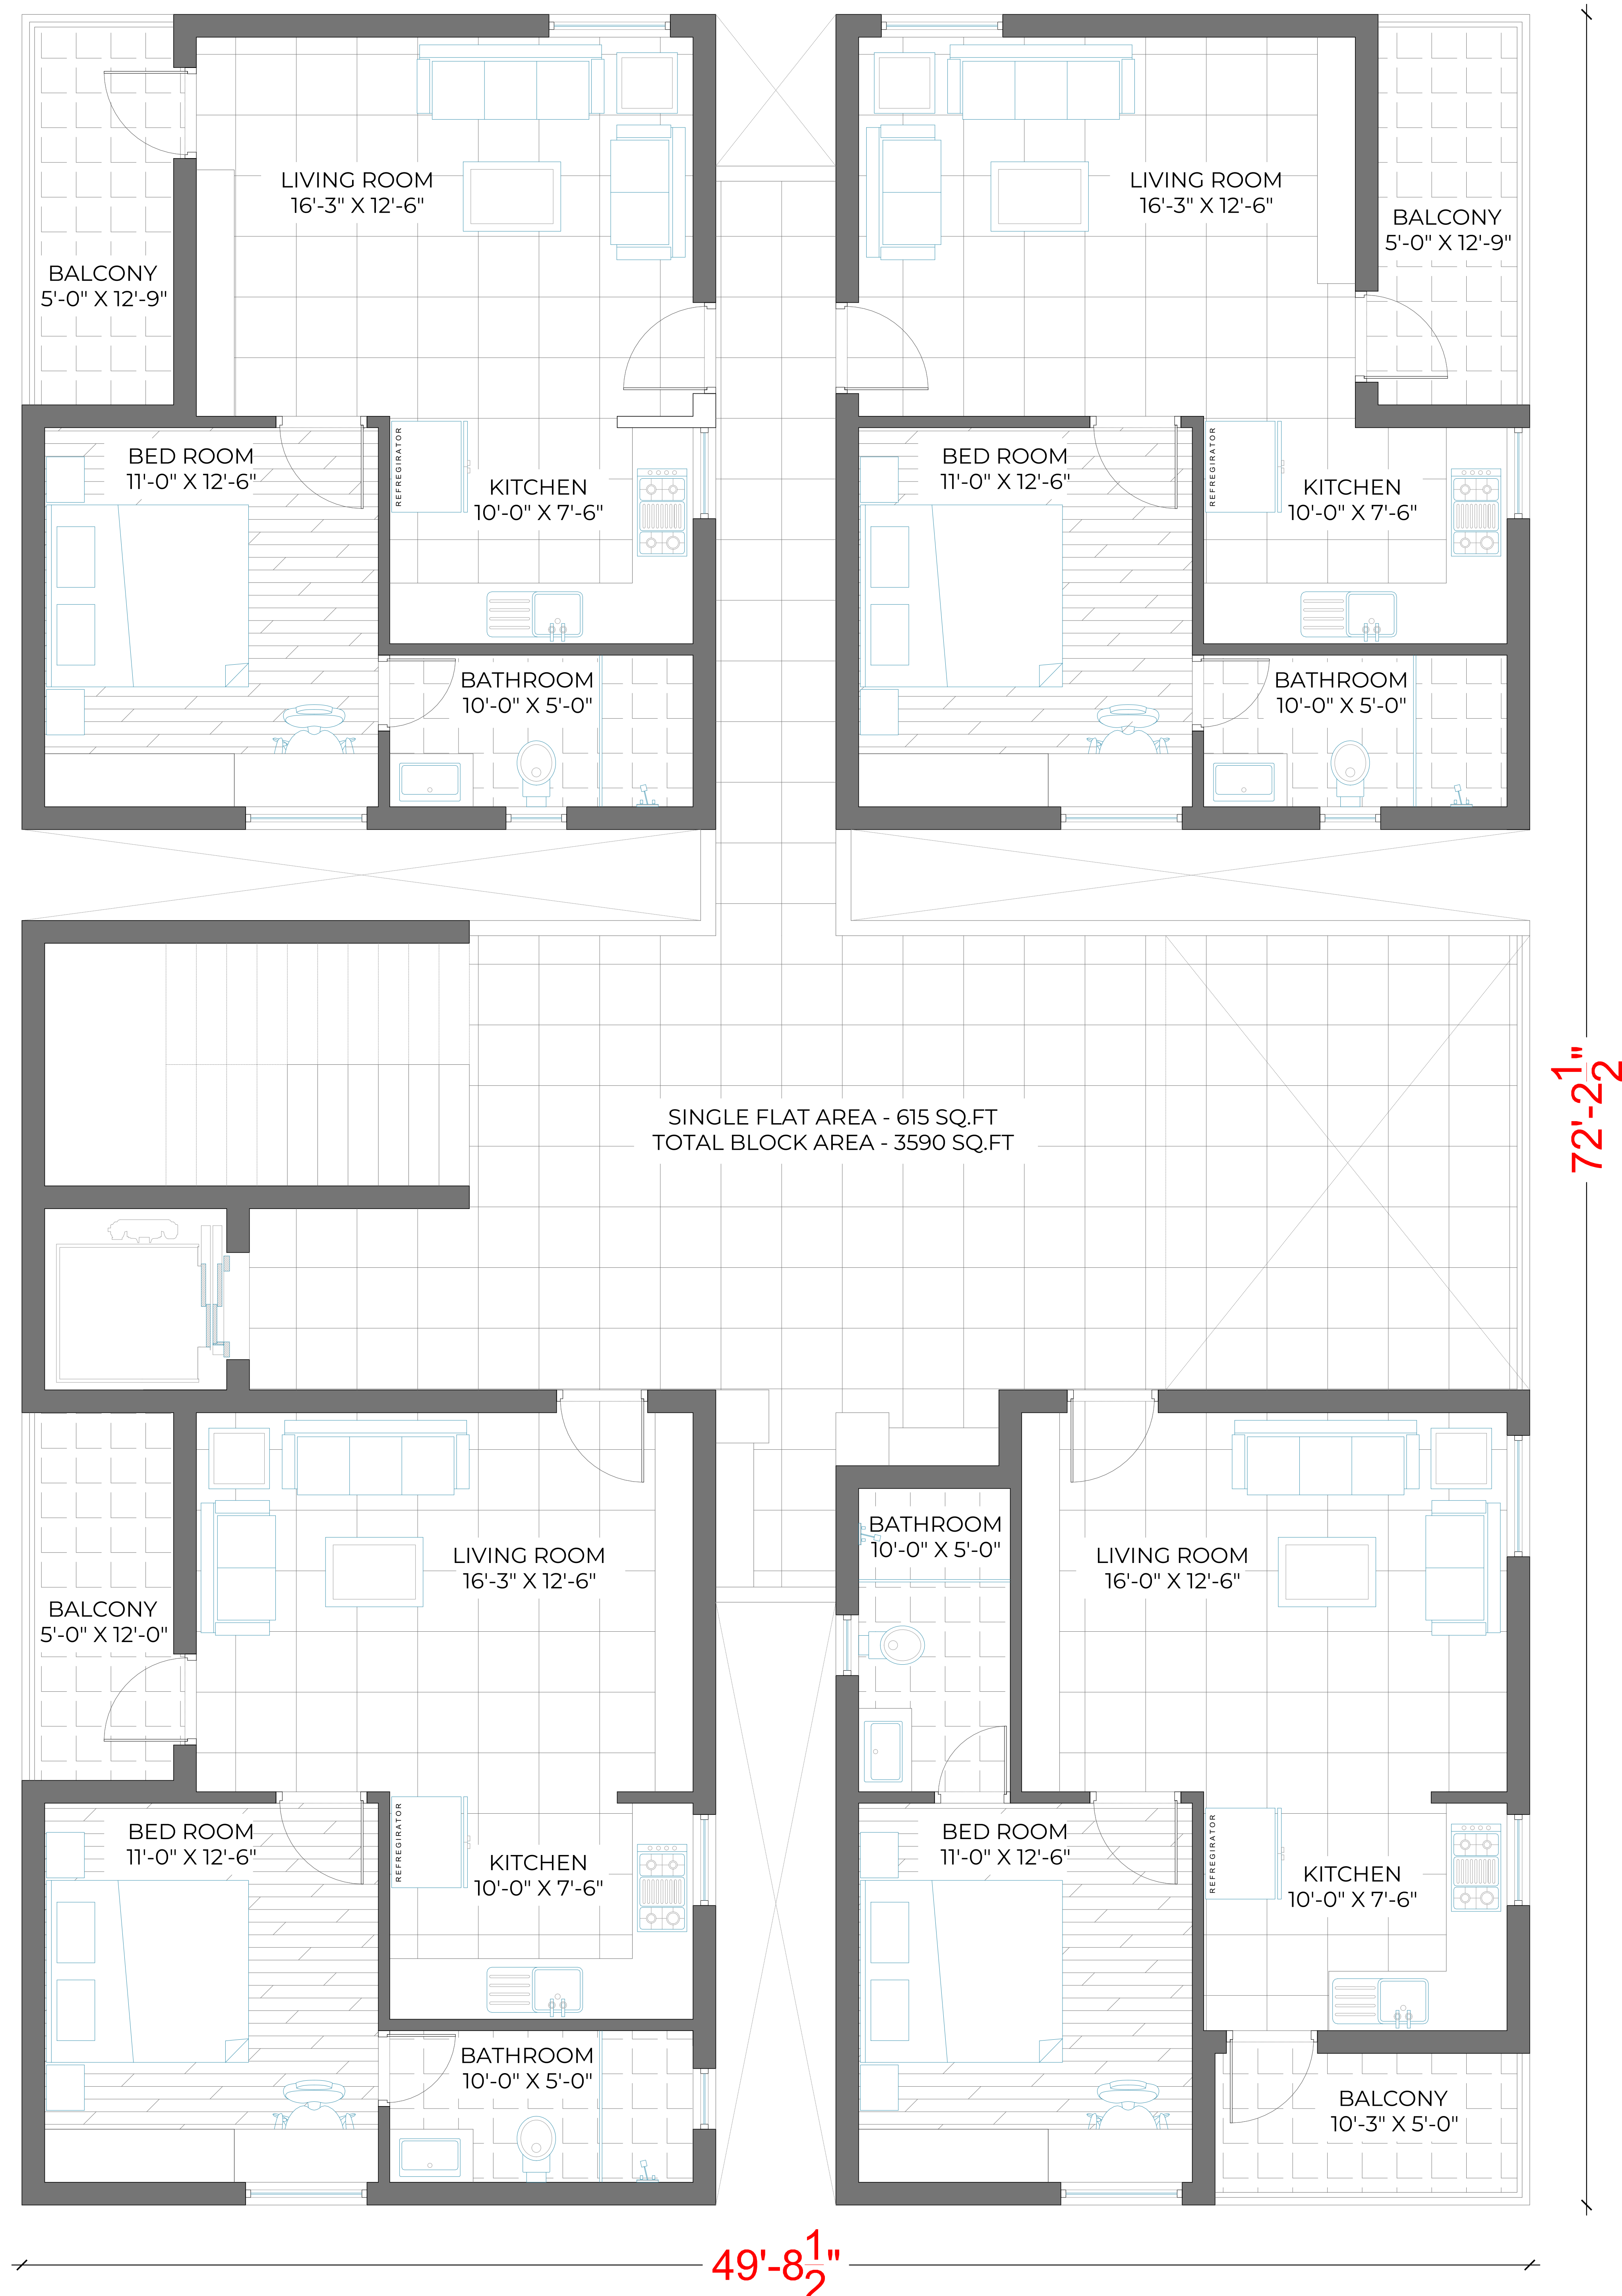

**DRAWING TITLE :** BLOCK B TYPICAL FLOOR PLAN

**PROJECT TITLE :** SERVICE APARTMENT @NALAGANDLA

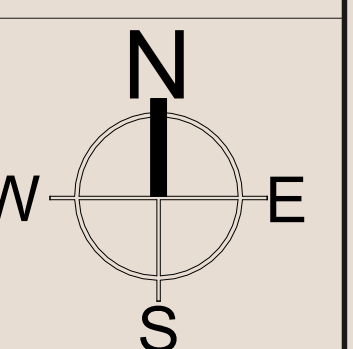

**DWG. No. :** -

**DWG. STG. :** DESIGN DEVELOPMENT

**CLIENT :** Mr.MAHENDAR REDDY

**LOCATION :** NALAGANDLA, HYD

**ARCHITECT :** CHANDRASHEKAR

**DRAWN BY :** AR.AJAYSAI

**SCALE :** NTS

**DATE :** 7-Apr-26

**REVISION :** 001

**APPROVED :** CSY


**COUNT OF TOTAL NO. OF DRWGS. ISSUED TO SITE / CLIENT :** 003



**NOTES :**


THIS DRAWING IS SUBJECT TO COPYRIGHT AND CANNOT BE COPIED WITHOUT ANY PRIOR WRITTEN CONSENT BY THE COPIER TO THE ARCHITECT FOR APPROVAL. THE CONTRACTOR SHALL VERIFY THE ALL DIMENSIONS IN DRAWING TO THE SITE IN RESPECTIVE SCALE. MENTIONED IN DRAWING AND DRAWING MUST BE REFERRED TO THE ARCHITECT IF ANY DISCREPANCIES ARE NOTICED IN DRAWING BEFORE COMMENCEMENT OR DURING EXECUTION.

1. ALL THE DIMENSIONS ARE IN IMPERIAL SCALE UNLESS AND UNTIL MENTIONED BY THE CONTRACTOR FOR CHANGE OF UNITS.
2. THE DRAWING SHOULD BE READ AND NOT BE MEASURED.
3. ANY DEVIATION FROM THE CONSTRUCTION DRAWINGS, THE CONTRACTOR/ SUB CONTRACTOR SHOULD GET AN APPROVAL FROM THE CONCERNED ARCHITECT OR ENGINEER BEFORE THE COMMENCEMENT OF CONSTRUCTION.
4. ALL ARCHITECTURAL DRAWINGS MUST BE REFERRED IN COORDINATION WITH STRUCTURAL DRAWINGS.

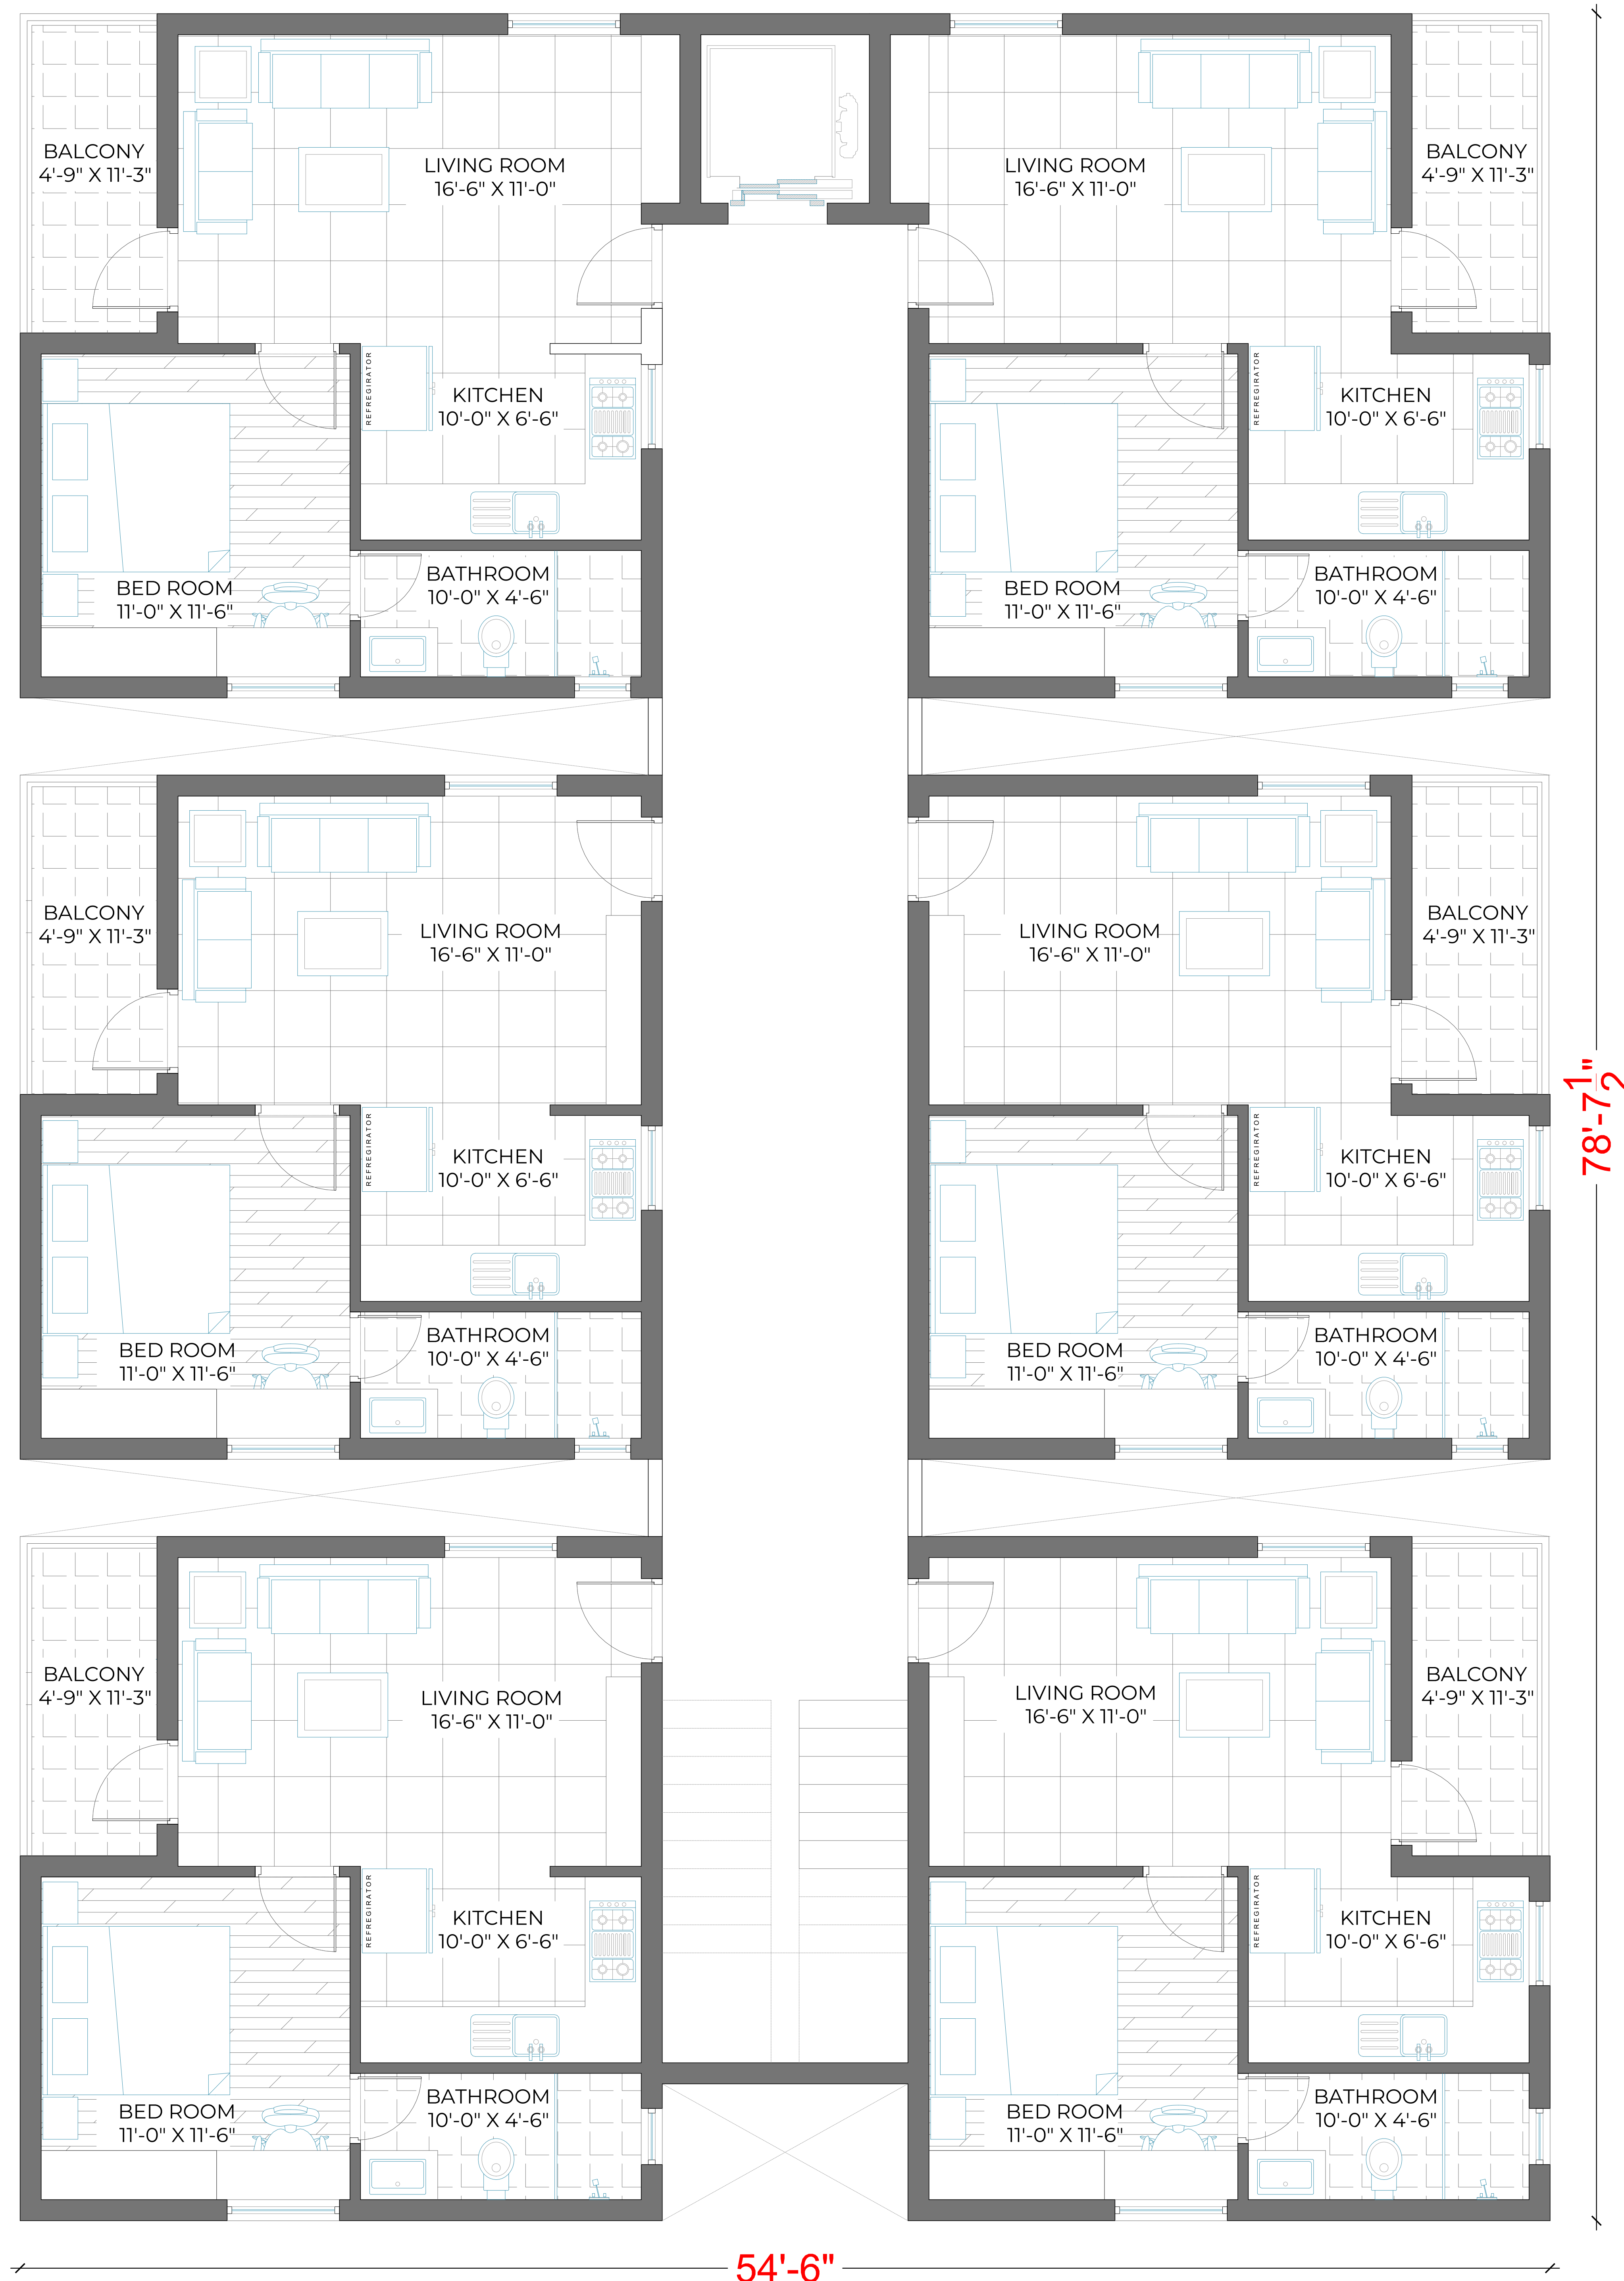

**DRAWING TITLE :** BLOCK C TYPICAL FLOOR PLAN

**PROJECT TITLE :** SERVICE APARTMENT @NALAGANDLA

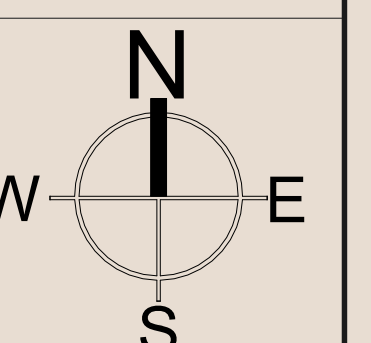

**DWG. No. :** -

**DWG. STG. :** DESIGN DEVELOPMENT

**CLIENT :** Mr.MAHENDAR REDDY

**LOCATION :** NALAGANDLA, HYD

**ARCHITECT :** CHANDRASHEKAR

**DRAWN BY :** AR.AJAYSAI

**SCALE :** NTS

**DATE :** 7-Apr-26

**REVISION :** 001

**APPROVED :** CSY


**COUNT OF TOTAL NO. OF DRWGS. ISSUED TO SITE / CLIENT :** 004



**NOTES :**

THIS DRAWING IS SUBJECT TO COPYRIGHT AND CANNOT BE COPIED WITHOUT ANY PRIOR WRITTEN CONSENT BY THE COPIER TO THE ARCHITECT FOR APPROVAL  
THE CONTRACTOR SHALL VERIFY THE ALL DIMENSIONS IN DRAWING TO THE SITE IN RESPECTIVE SCALE. MENTIONED IN DRAWING AND DRAWING MUST BE REFERRED TO THE ARCHITECT IF ANY DISCREPANCIES ARE NOTICED IN DRAWING BEFORE COMMENCEMENT OR DURING EXECUTION .

1. ALL THE DIMENSIONS ARE IN IMPERIAL SCALE UNLESS AND UNTIL MENTIONED BY THE CONTRACTOR FOR CHANGE OF UNITS.
2. THE DRAWING SHOULD BE READ AND NOT BE MEASURED.
3. ANY DEVIATION FROM THE CONSTRUCTION DRAWINGS, THE CONTRACTOR/ SUB CONTRACTOR SHOULD GET AN APPROVAL FROM THE CONCERNED ARCHITECT OR ENGINEER BEFORE THE COMMENCEMENT OF CONSTRUCTION.
4. ALL ARCHITECTURAL DRAWINGS MUST BE REFERRED IN COORDINATION WITH STRUCTURAL DRAWINGS.

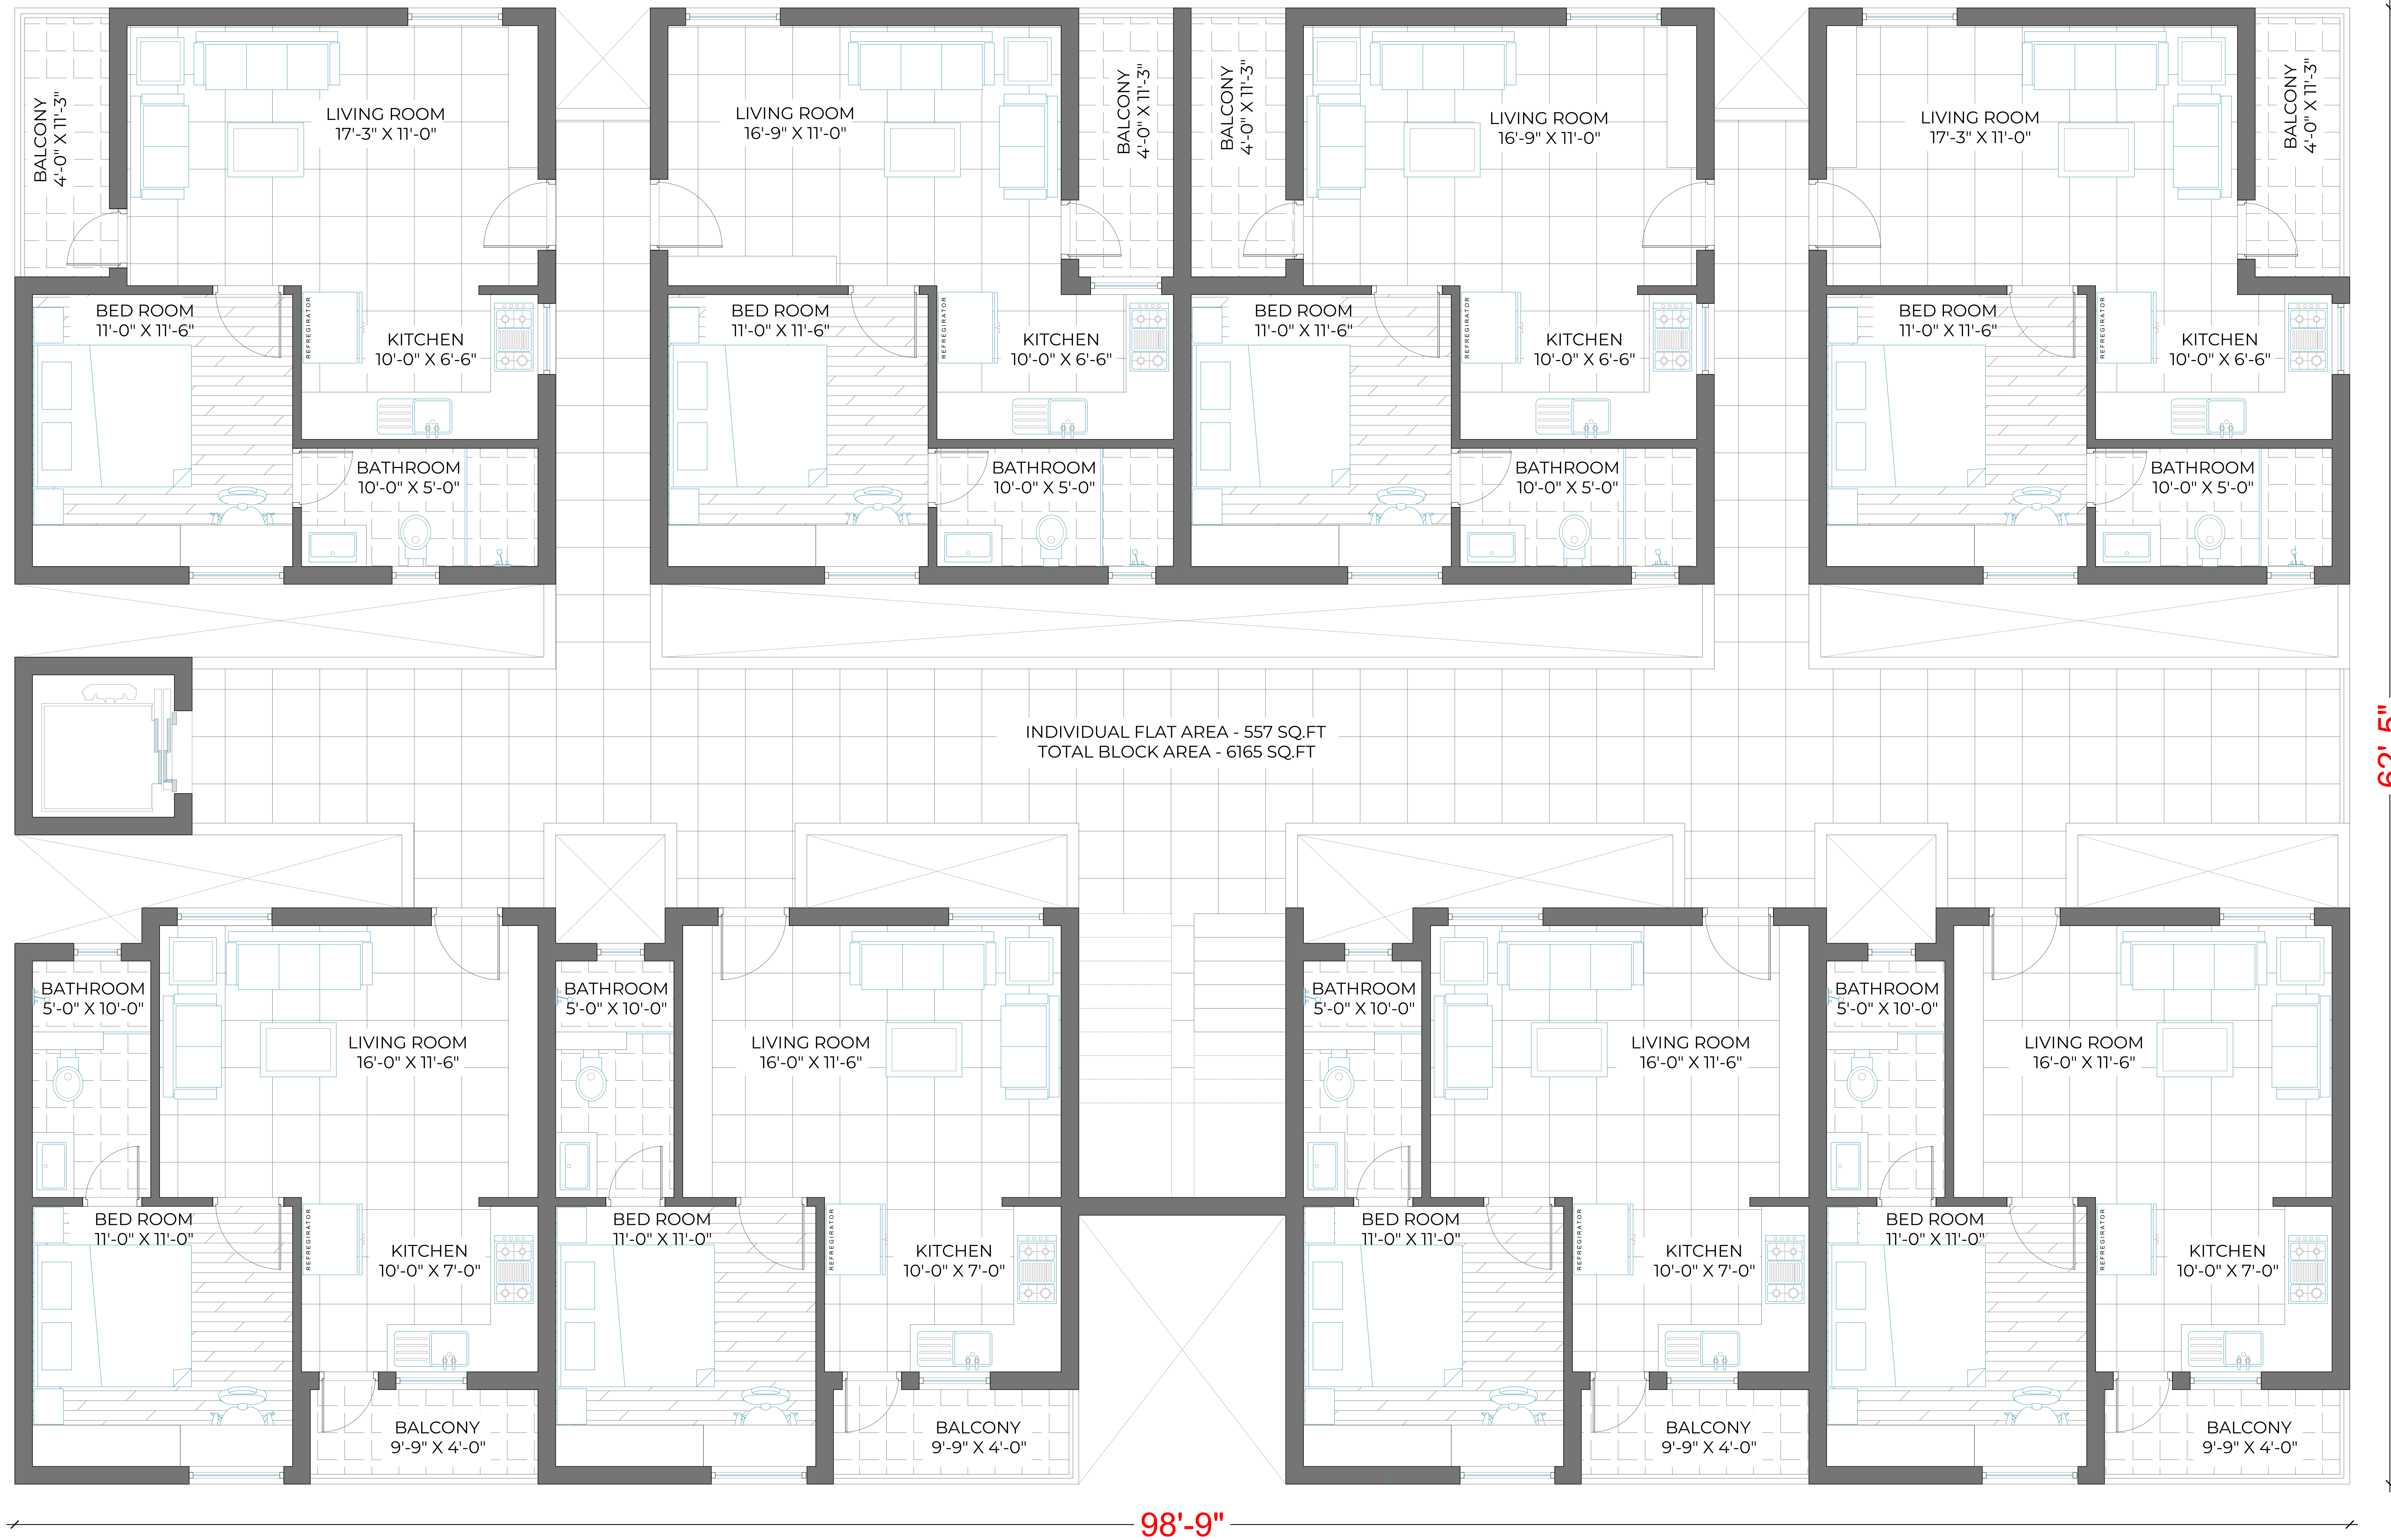


62'-5"

98'-9"

**DRAWING TITLE : BLOCK D TYPICAL FLOOR PLAN**

**PROJECT TITLE : SERVICE APARTMENT @NALAGANDLA**

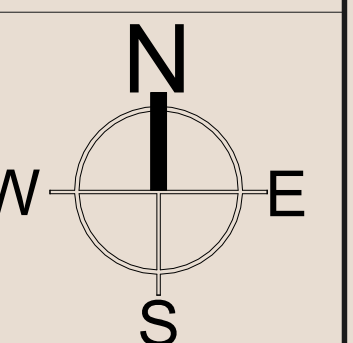

DWG. No. : -

DWG. STG. : DESIGN DEVELOPMENT

CLIENT : Mr.MAHENDAR REDDY

LOCATION : NALAGANDLA, HYD

ARCHITECT: CHANDRASHEKAR

DRAWN BY: AR.AJAYSAI

SCALE NTS

DATE 7-Apr-26

REVISION : 001

APPROVED: CSY


COUNT OF TOTAL NO. OF DRWGS. ISSUED TO SITE / CLIENT : 005



**NOTES :**


THIS DRAWING IS SUBJECT TO COPYRIGHT AND CANNOT BE COPIED WITHOUT ANY PRIOR WRITTEN CONSENT BY THE ARCHITECT FOR APPROVAL.  
THE CONTRACTOR SHALL VERIFY THE ALL DIMENSIONS IN DRAWING TO THE SITE IN RESPECTIVE SCALE. MENTIONED IN DRAWING AND DRAWING MUST BE REFERRED TO THE ARCHITECT IF ANY DISCREPANCIES ARE NOTICED IN DRAWING BEFORE COMMENCEMENT OR DURING EXECUTION.

1. ALL THE DIMENSIONS ARE IN IMPERIAL SCALE UNLESS AND UNTIL MENTIONED BY THE CONTRACTOR FOR CHANGE OF UNITS.
2. THE DRAWING SHOULD BE READ AND NOT BE MEASURED.
3. ANY DEVIATION FROM THE CONSTRUCTION DRAWINGS, THE CONTRACTOR/ SUB CONTRACTOR SHOULD GET AN APPROVAL FROM THE CONCERNED ARCHITECT OR ENGINEER BEFORE THE COMMENCEMENT OF CONSTRUCTION.
4. ALL ARCHITECTURAL DRAWINGS MUST BE REFERRED IN COORDINATION WITH STRUCTURAL DRAWINGS.

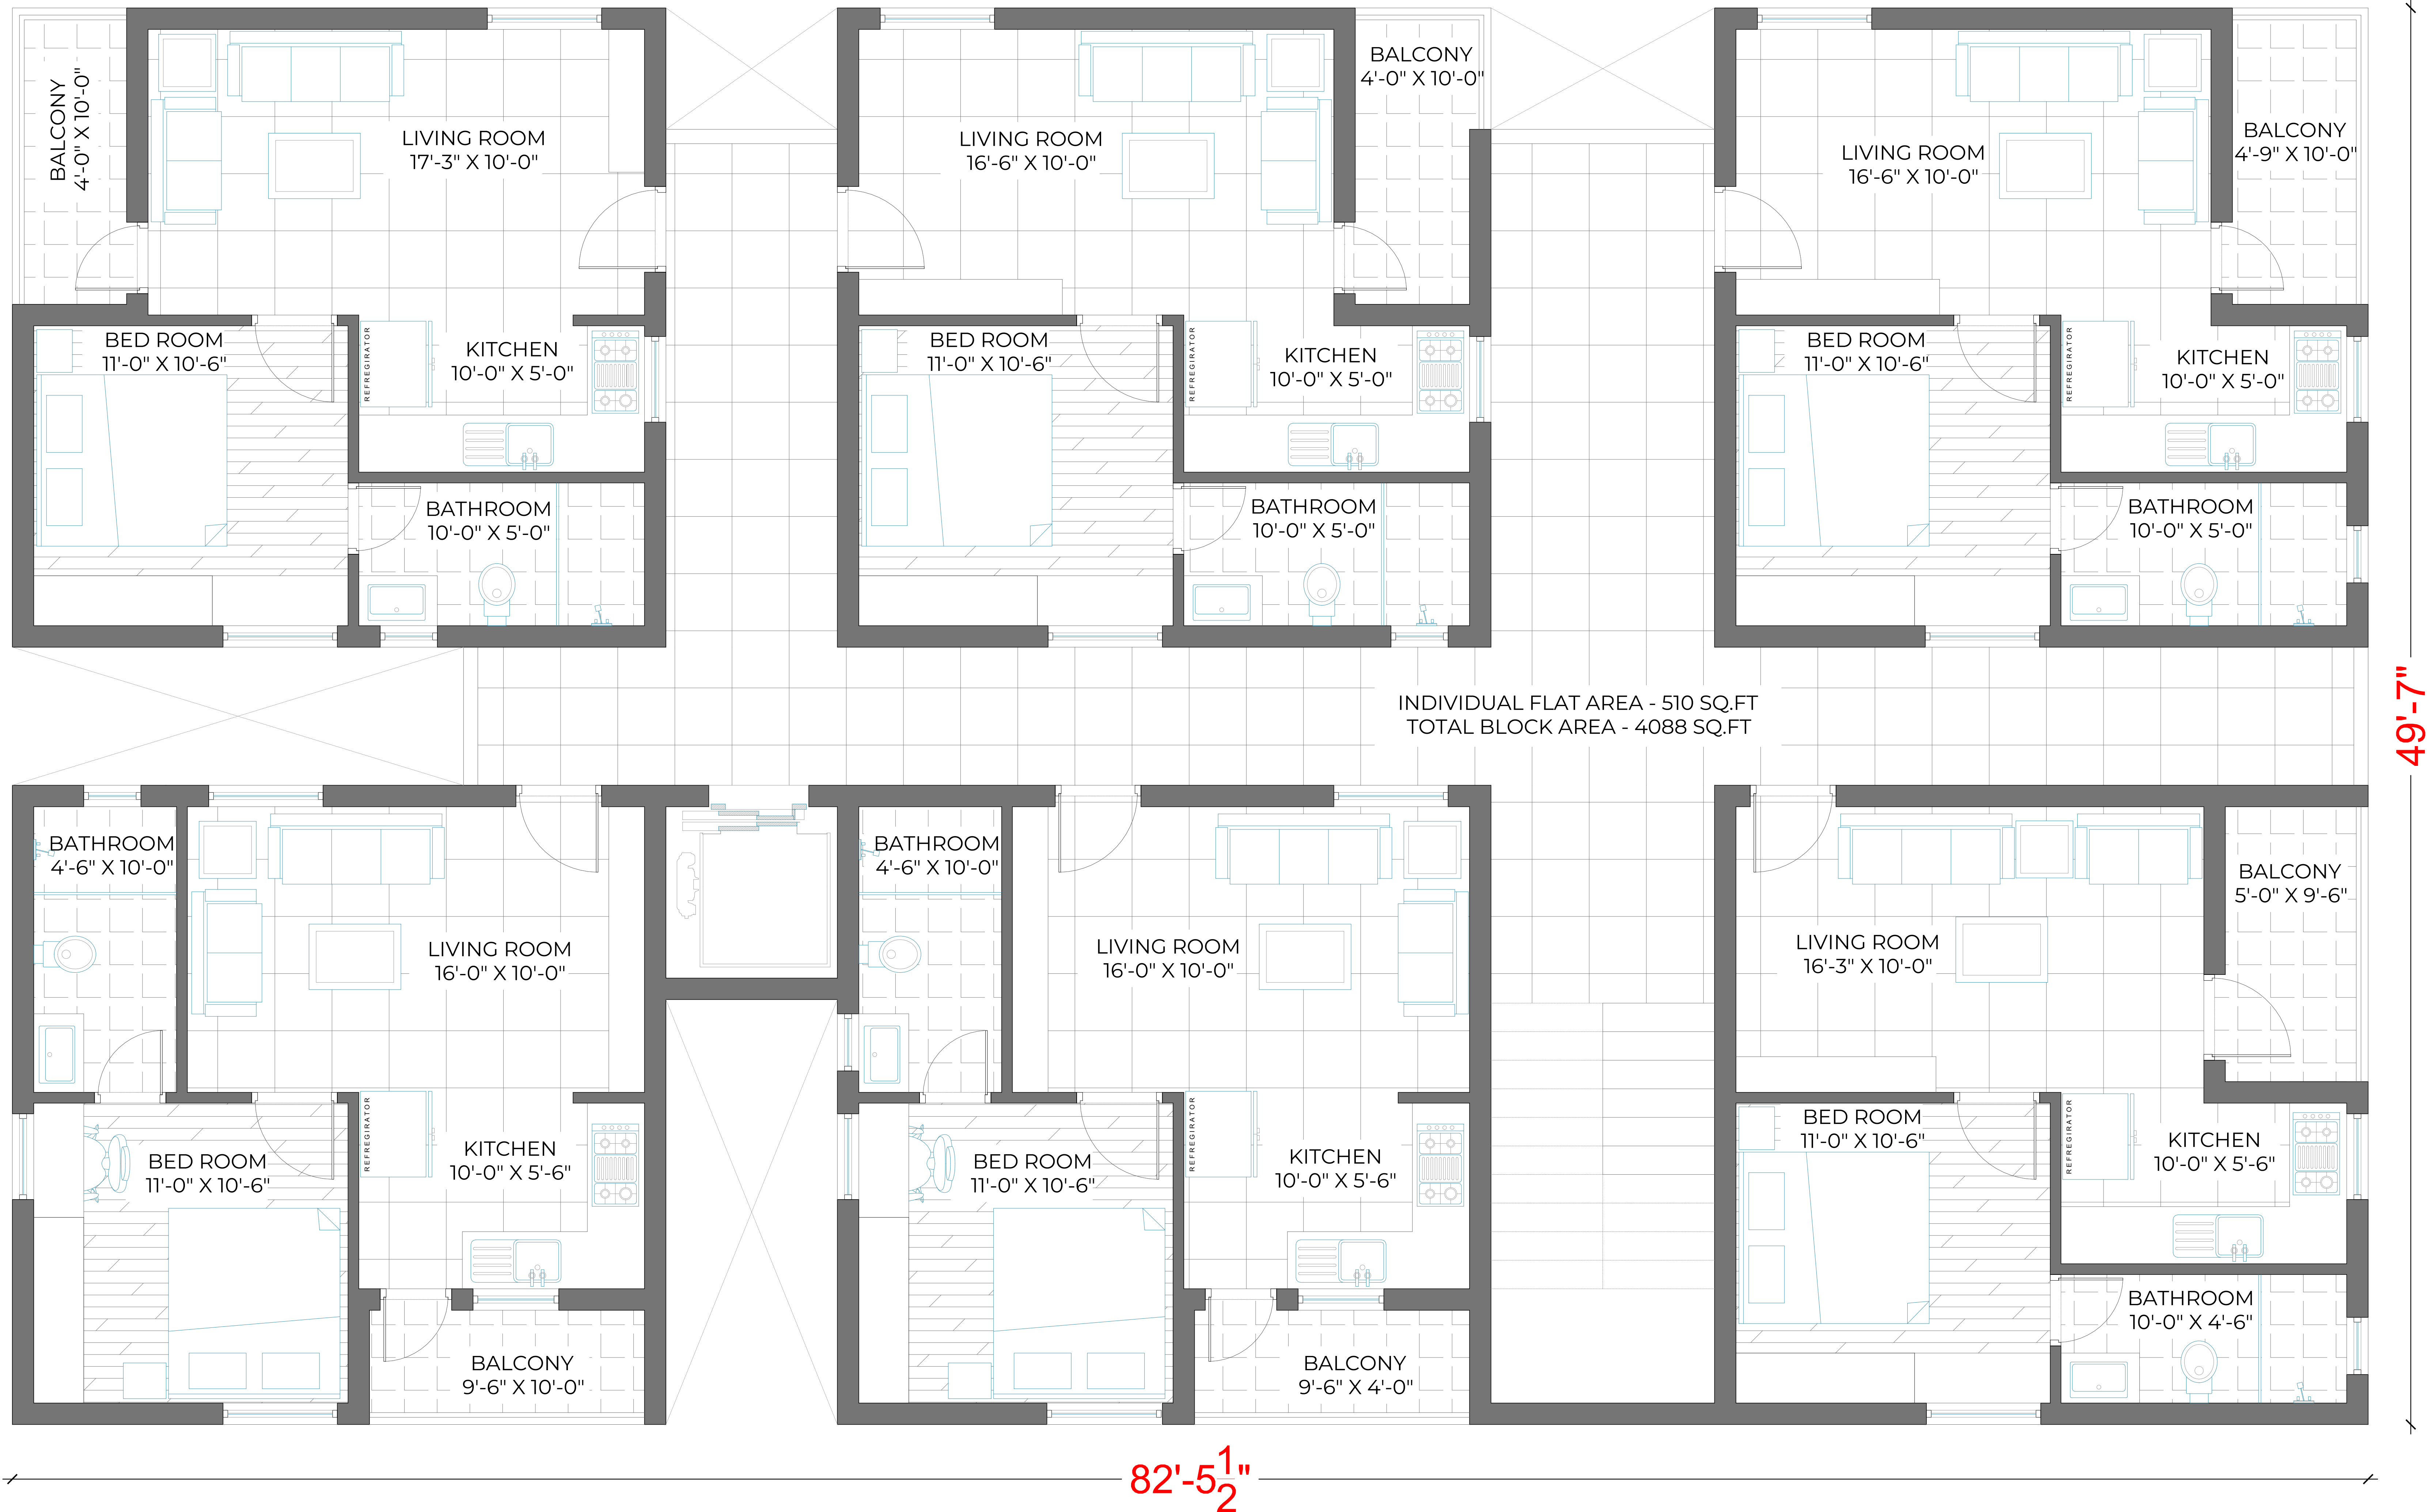

**DRAWING TITLE :** BLOCK E TYPICAL FLOOR PLAN

**PROJECT TITLE :** SERVICE APARTMENT @NALAGANDLA

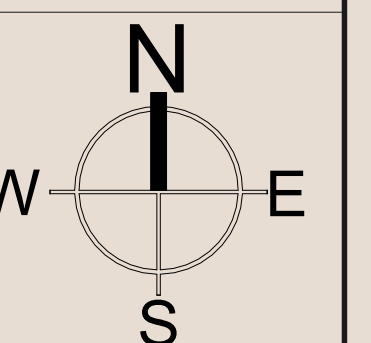

**DWG. No. :** -

**DWG. STG. :** DESIGN DEVELOPMENT

**CLIENT :** Mr.MAHENDAR REDDY **LOCATION :** NALAGANDLA,HYD

**ARCHITECT:** CHANDRASHEKAR **DRAWN BY:** AR.AJAYSAI

**SCALE** NTS **DATE** 7-Apr-26 **REVISION :** 001 **APPROVED:** CSY

**COUNT OF TOTAL NO. OF DRWGS. ISSUED TO SITE / CLIENT :** 006